A17B-01地块地块经济技术指标

项目				数值	单位	备注
总用地面积				19517.55	平方米	
总建筑面积				53226.87	平方米	
地上总建筑面积				53226.87	平方米	
其中	地上计容面积			48793.88	平方米	
	其中	商品房		47783.77	平方米	
		公共服务配套建筑面积		993.41	平方米	
		其中	居民委员会	200.00	平方米	50㎡/1000人，最小200㎡
			老年活动室	200.00	平方米	60㎡/1000人，最小200㎡
			物业管理	163.41	平方米	总建面2‰，最小120㎡
			业委会	30.00	平方米	
			生活服务点	100.00	平方米	20㎡/1000人，最小100㎡
			文化活动室（含10㎡活动室垃圾房）	100.00	平方米	30㎡/1000人，最小100㎡
			社区大堂	200.00	平方米	1处位于6#楼首层，1处位于1#楼首层
		地下室出地面电梯		16.70	平方米	
	地上不计容建筑面积			4432.99	平方米	
		商品房超低能耗奖励		1434.00	平方米	
		风雨连廊		740.00	平方米	
		架空层		1345.00	平方米	含智能快递柜36.00㎡，设置于1号楼
		开闭所/配电间		424.00	平方米	
		屋顶机房		373.09	平方米	
		饰面层建筑面积		91.40	平方米	
		还建生活垃圾分类收集房		25.50	平方米	南侧小区配建
容积率				2.50		
建筑密度				26.15	%	
绿地率				35.00	%	
户数				430	户	
人数				1376	人	3.2人/户

项目结合绿地区域设置儿童游戏场不小于60平方米，健身点不小于300平方米，具体结合景观二次深化设置。

图 例

▬ ▬	规划用地红线	➡	出入口
▬	新建建筑	▲	住宅出入口
4F/1D	地上层数／地下层数	═	消防车道
H=13.5	建筑规划高度	⋈	消防车登高操作场地
③#	楼栋号	▨	绿化填充
▼6.770	场地、道路标高	✲	集中绿地
±0.00(7.60)	绝对标高	─□─	围墙
X=90250.632 Y=91419.352	定位坐标		

说明：
1. 图中的标高和尺寸均以米为单位；
2. 本图中F表示建筑地上层数；
3. 图中景观为示意，详景观二次深化设计。

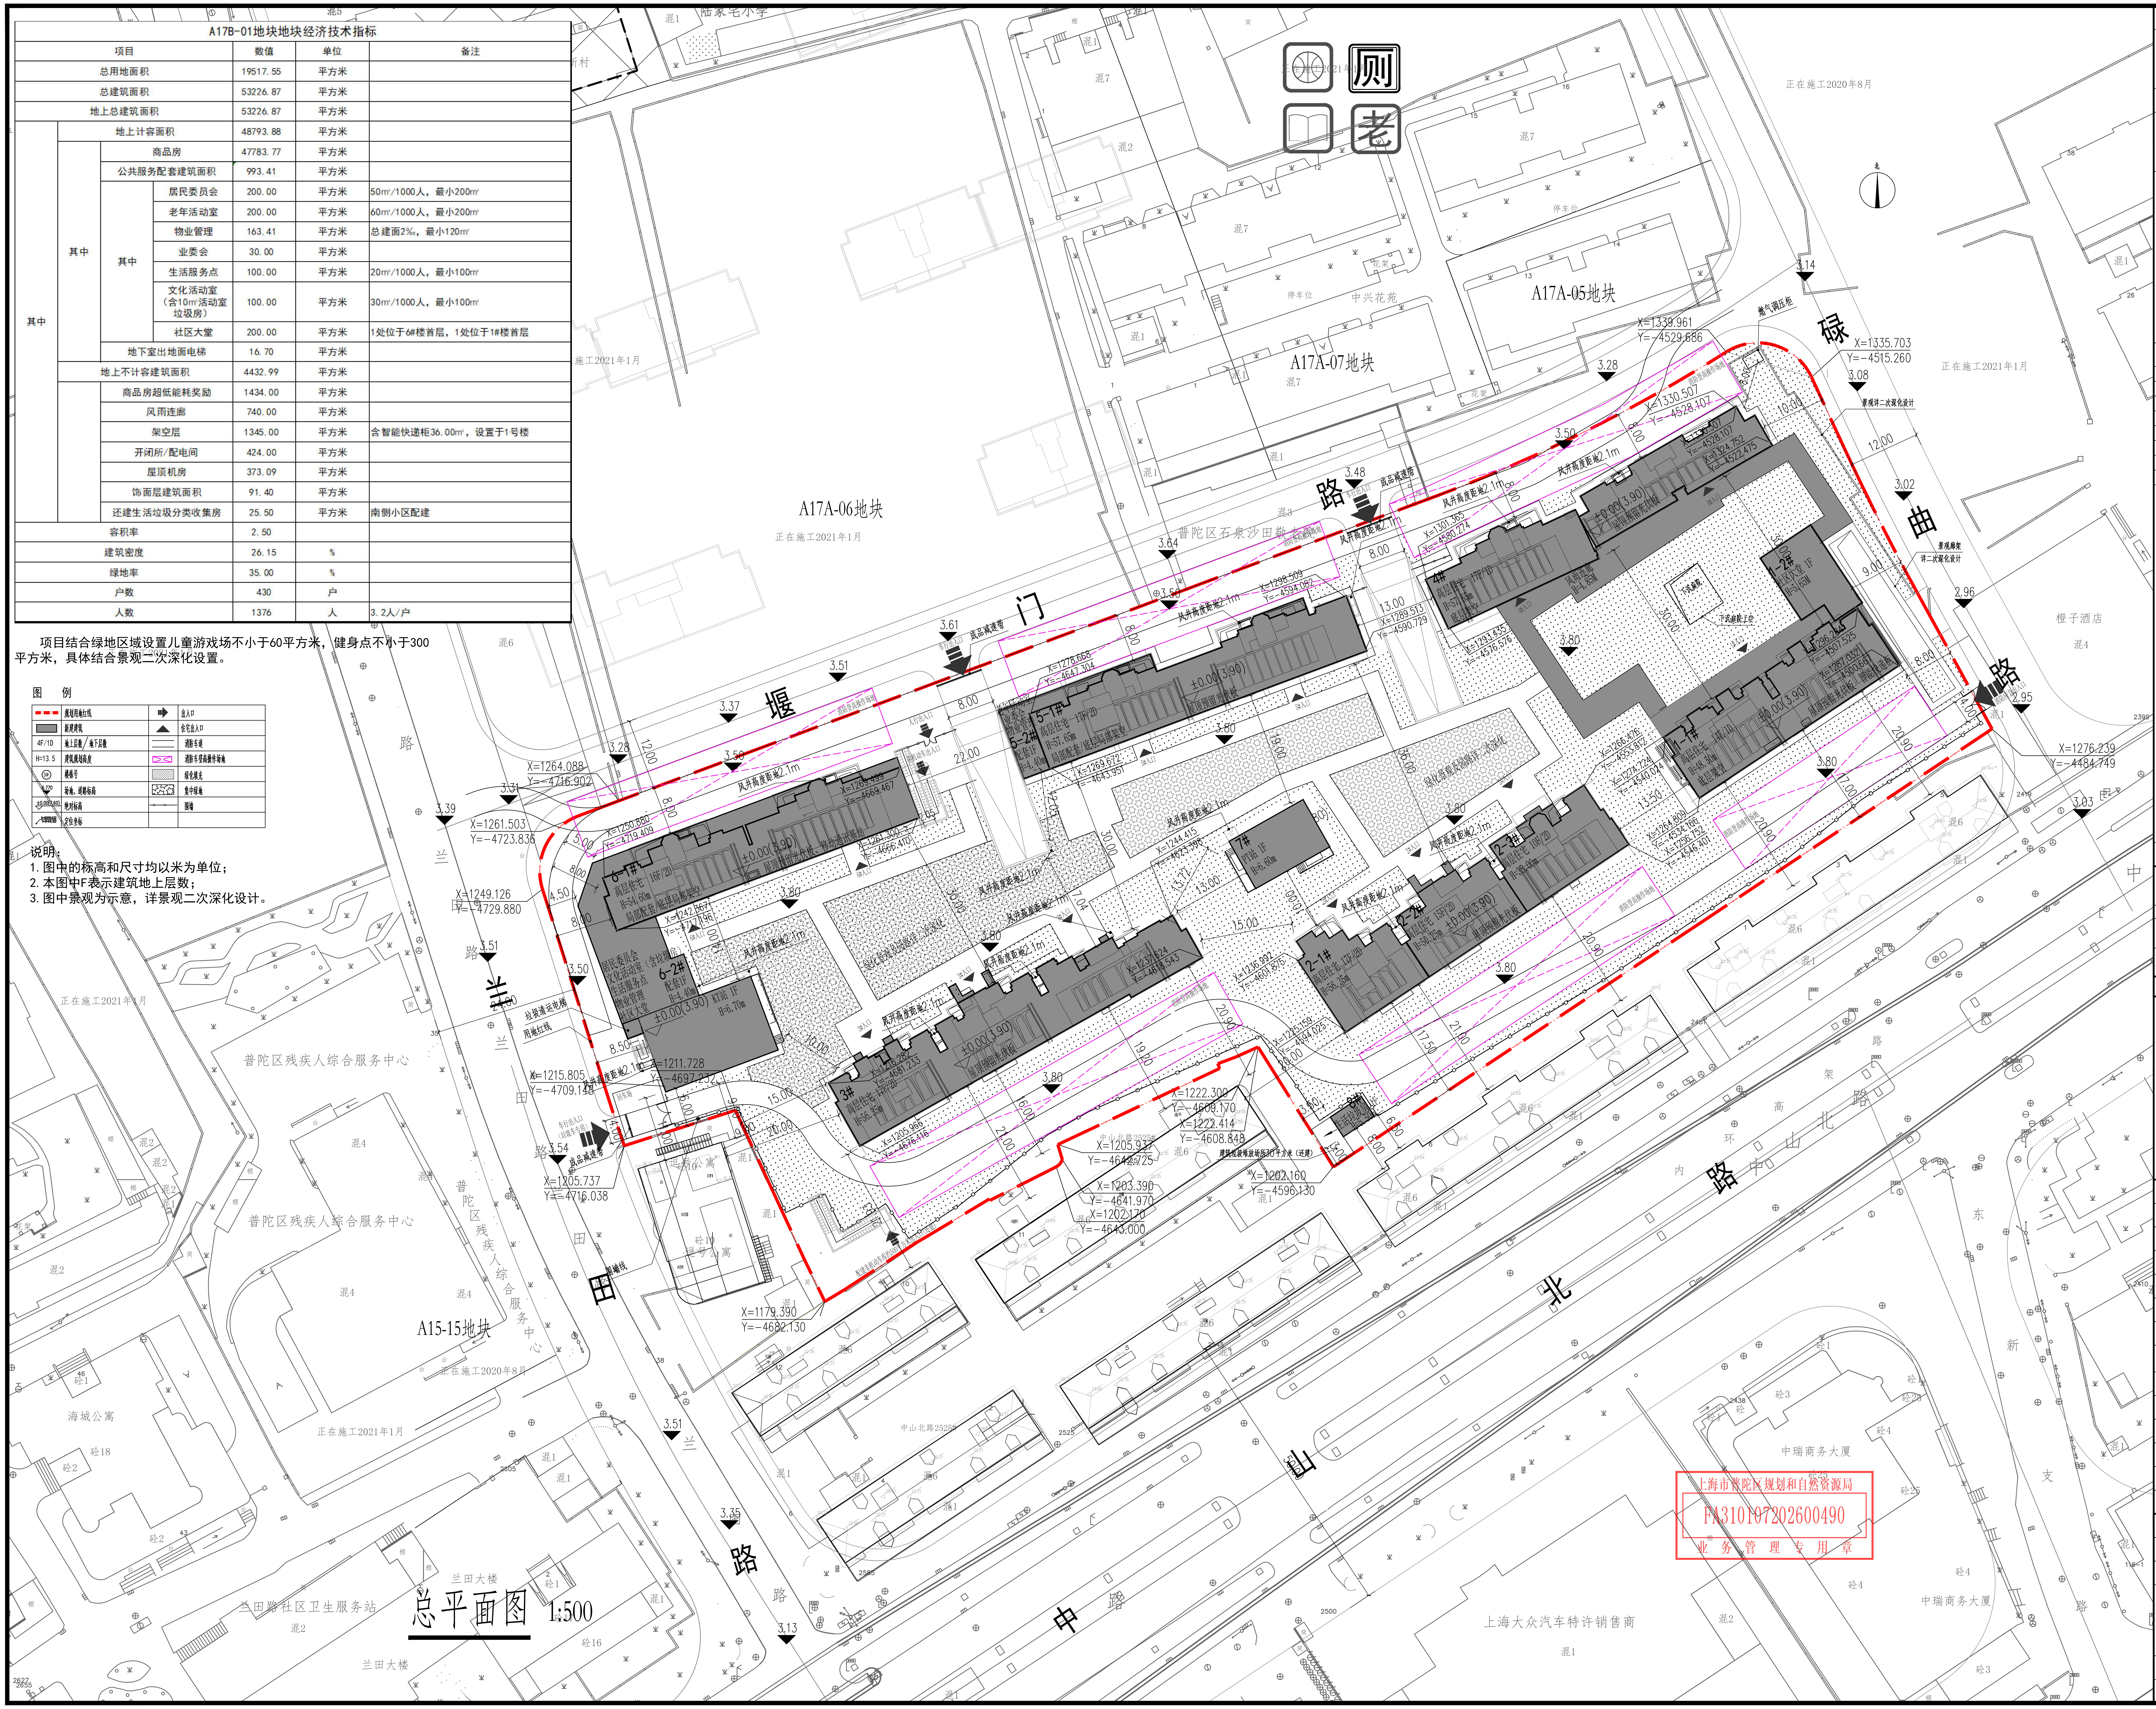

总平面图 1:500

上海市普陀区规划和自然资源局
FA310107202600490
业 务 管 理 专 用 章

项目名称 Project
普陀区W060401单元A17B-01地块项目

工程设计出图专用章(电子)
资质证书号：A131A01681
有效期至：2025年06月25日

业 主 Client
上海锦通达置业有限公司

中华人民共和国一级注册建筑师
姓 名：赵亮
注册号：3100211-206
有效期：至2027年05月27日
电子

出图记录 Issue Notes

版次Rev.	日 期 Date	设 计 Designed by
A	2026.08.12	武帅

比 例 Scale

TIANHUA天华
www.thape.com
上海天华建筑设计有限公司
Tian Hua Architecture Planning & Engineering Limited
中国 上海市 中山西路1800号 兆丰环球大厦27楼
27F, 1800 Zhongshan West Rd. Shanghai 200235,PRC
设计证号 Licence NO. A131A01681

所有施工图蓝图须加盖本公司施工图用图章后为有效施工图

审 定 Authorized	丁纯		
审 核 Approved by	赵亮		
设计总负责 Project director	赵亮		
专业负责人 Discipline Responsible	赵亮		
校 对 Checked by	任晓涵		
设 计 Designed by	武帅		
制 图 Drawn by	武帅		
会 签 Comfirmed by			
建 筑 Architecture		强 电 Electricity	
结 构 Structure		弱 电 Telecom	
给 排 水 WS&D		暖 通 HVAC	
燃 气 Gas		动 力 Dynamics	
室 内 Interior		景 观 Landscape	
人 防			
项目编号 Porject No.	TH26134501	设计类别 Category	土建
专 业 Discipline	建筑	设计阶段 Status	
设计子项 Project Subdivision	总图		
图纸名称 Drawing Title	总平面图		
日 期 Date	2026.08.12		
图纸编号 Drawing No.	TY-A0201A		

上海中船九院工程咨询有限公司
施工图纸审查专用章(电子)
审查机构编号：09038