A17B-01地块地块经济技术指标

项目				数值	单位	备注
总用地面积				19517.55	平方米	
总建筑面积				81330.87	平方米	
地上总建筑面积				53226.87	平方米	
其中	地上计容面积			48793.88	平方米	
	其中	商品房		47783.77	平方米	
		公共服务配套建筑面积		993.41	平方米	
		其中	居民委员会	200.00	平方米	50m²/1000人，最小200m²
			老年活动室	200.00	平方米	60m²/1000人，最小200m²
			物业管理	163.41	平方米	总建面2‰，最小120m²
			业委会	30.00	平方米	
			生活服务点	100.00	平方米	20m²/1000人，最小100m²
			文化活动室（含10m²活动室垃圾房）	100.00	平方米	30m²/1000人，最小100m²
			社区大堂	200.00	平方米	1处位于6#楼首层，1处位于1#楼首层
		地下室出地面电梯		16.70	平方米	
	地上不计容建筑面积			4432.99	平方米	
		商品房超低能耗奖励		1434.00	平方米	
		风雨连廊		740.00	平方米	
		架空层		1345.00	平方米	含智能快递柜36.00m²，设置于1号楼
		开闭所/配电间		424.00	平方米	
		屋顶机房		373.09	平方米	
		饰面层建筑面积		91.40	平方米	
		还建生活垃圾分类收集房		25.50	平方米	南侧小区配建
地下总建筑面积				28104.00	平方米	含还建水泵房
其中	车库及配套			27509.00	平方米	含地下会所
	还建非机动车库			500.00	平方米	给南侧小区配建
	生活垃圾分类收集房			35.00	平方米	
	建筑垃圾房			30.00	平方米	
	大件垃圾房			30.00	平方米	
容积率				2.50		
建筑密度				26.15	%	
绿地率				35.00	%	
户数				425	户	
人数				1360	人	3.2人/户
非机动车停车位				421	个	自然车位数357辆，折算后421辆，80%以上为充电车位
机动车停车位				526	个	共561个停车位，折合526个换算当量
其中	地上机动车停车位			0	个	
	地下机动车停车位			526	个	

项目结合绿地区域设置儿童游戏场不小于60平方米，健身点不小于300平方米，具体结合景观二次深化设置。

图　例

━ ━ ━	规划用地红线	➡	出入口
▨	新建建筑	▲	住宅出入口
4F/1D	地上层数/地下层数	═	消防车道
H=13.5	建筑规划高度	⊠	消防车登高操作场地
(3#)	楼栋号	▩	绿化填充
6.770 ▼	场地、道路标高	✲	集中绿地
±0.00(7.60)	绝对标高	─□─□─	围墙
X=90250.632 Y=91419.352	定位坐标	- - - -	地下室外轮廓线

说明：
1. 图中的标高和尺寸均以米为单位；
2. 本图中F表示建筑地上层数；
3. 图中景观为示意，详景观二次深化设计。
4. 本图中坐标和标高与用地红线坐标系统均根据甲方提供的设计条件资料绘制而成，坐标及高程系统均同甲方提供征地红线图。
5. 平面坐标系采用本图中采用上海坐标系。
6. 高程采用吴淞高程系。
7. 停车位含会所停车位及社区配套停车位，具体位置以交通主管部门意见为准。

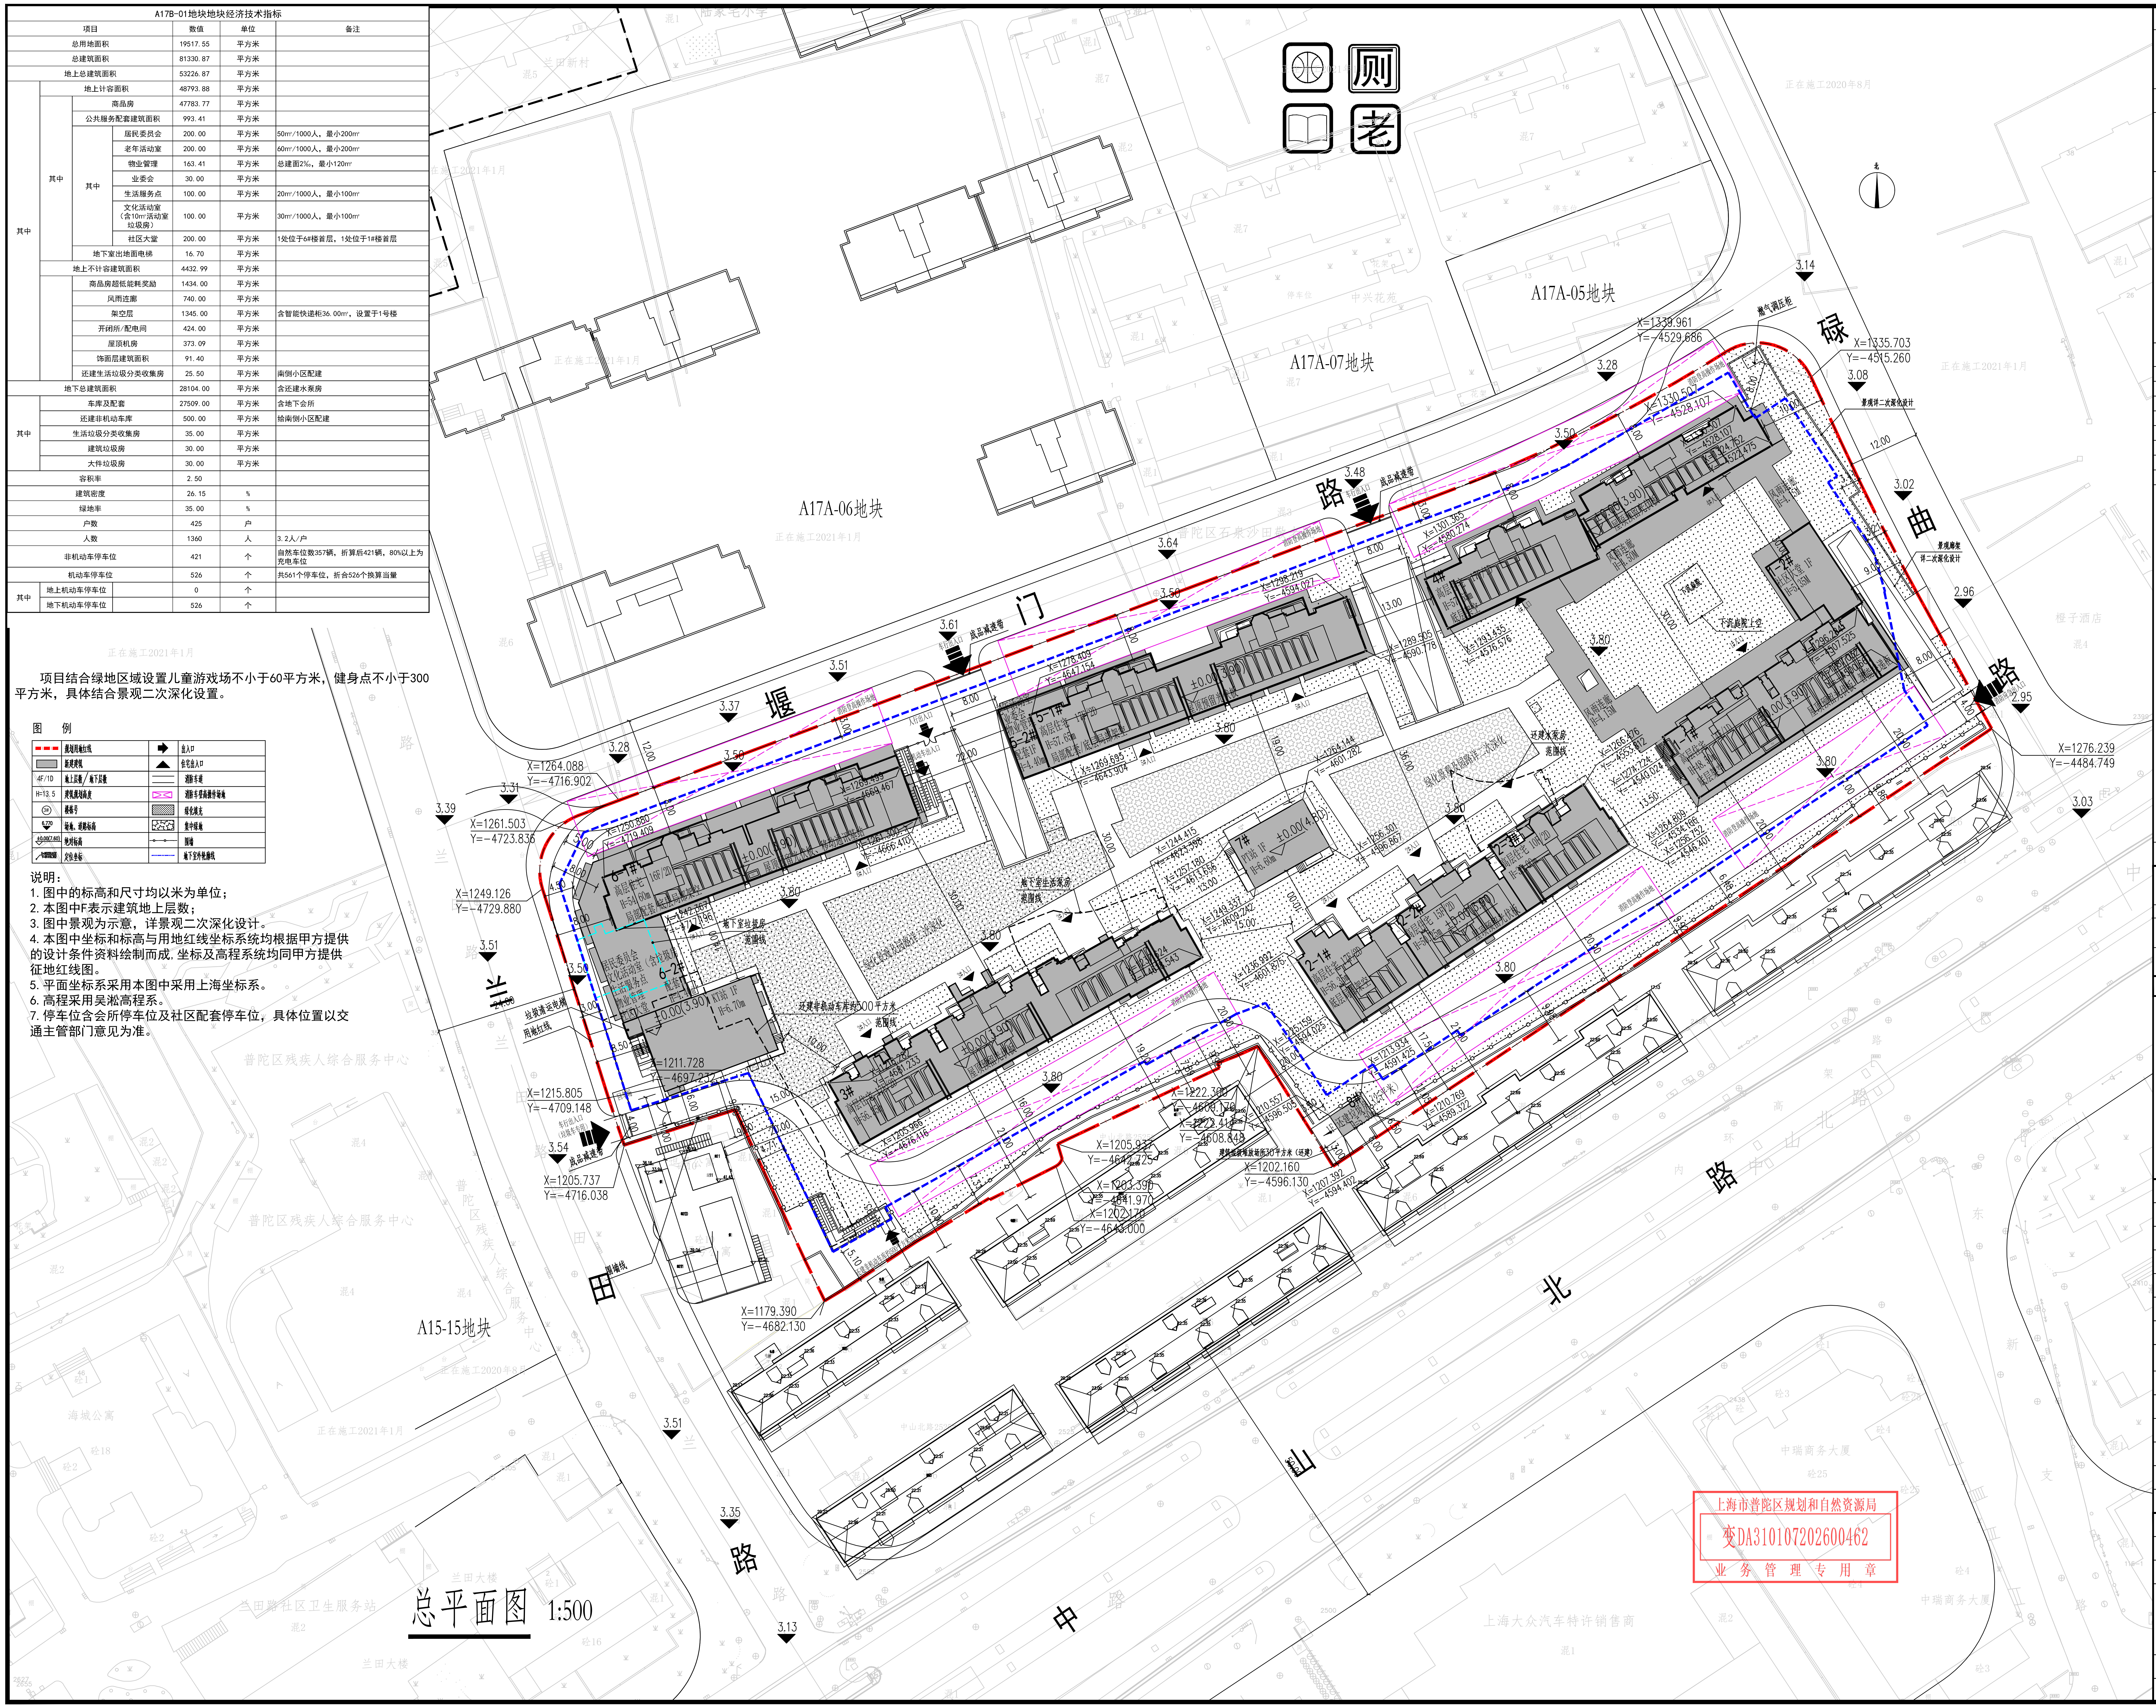
A17A-06地块
A17A-07地块
A17A-05地块
A15-15地块
堰
门
路
绿
曲
路
兰
田
路
中
山
北
路
普陀区残疾人综合服务中心
中瑞商务大厦
上海大众汽车特许销售商
正在施工2021年1月
1#
2-1#
2-2#
3#
4#
5-1#
5-2#
6-1#
6-2#
7#
8#
X=1339.961
Y=−4529.686
X=1335.703
Y=−4515.260
X=1276.239
Y=−4484.749
X=1264.088
Y=−4716.902
X=1261.503
Y=−4723.835
X=1249.126
Y=−4729.880
X=1215.805
Y=−4709.148
X=1205.737
Y=−4716.038
X=1179.390
Y=−4682.130
X=1202.160
Y=−4596.130
3.14
3.28
3.08
3.50
3.48
3.64
3.61
3.51
3.37
3.39
3.31
3.54
3.02
2.96
2.95
3.03
3.80
3.51
3.35
3.13
北

总平面图　1:500

上海市普陀区规划和自然资源局
变DA310107202600462
业务管理专用章

项目名称 Project	普陀区W060401单元A17B-01地块项目
业　主 Client	上海锦通达置业有限公司

资质证书号：A131A01681
有效期至：2029年06月25日

中华人民共和国一级注册建筑师
姓　名：赵亮
注册号：3100211-206
有效期：至2027年05月27日
电子

出图记录 Issue Notes

版次Rev.	日　期 Date	设　计 Designed by

比　例 Scale	

TIANHUA天华

www.thape.com

上海天华建筑设计有限公司
Tian Hua Architecture Planning & Engineering Limited

中国　上海市　中山西路1800号　兆丰环球大厦27楼
27F, 1800 Zhongshan West Rd. Shanghai 200235,PRC
设计证号 Licence NO. A131A01681

所有施工图蓝图须加盖本公司施工图用图章后为有效施工图

审　定 Authorized	丁纯		
审　核 Approved by	赵亮		赵亮
设计总负责 Project director	赵亮		赵亮
专业负责人 Discipline Responsible	赵亮		赵亮
校　对 Checked by	任晓涵		任晓涵
设　计 Designed by	武帅		
制　图 Drawn by	武帅		
会　签 Comfirmed by			
建　筑 Architecture		强　电 Electricity	
结　构 Structure		弱　电 Telecom	
给排水 WS&D		暖　通 HVAC	
燃　气 Gas		动　力 Dynamics	
室　内 Interior		景　观 Landscape	
人　防			
项目编号 Porject No.	TH26134501	设计类别 Category	土建
专　业 Discipline	建筑	设计阶段 Status	
设计子项 Project Subdivision	总图		
图纸名称 Drawing Title	总平面图		
日　期 Date	2026.08		
图纸编号 Drawing No.	TY-A0201A		